ОФИС ДИЗАЙНИ

ИЛИҚ МИНИМАЛИЗМ

13,5 м² · 3,95 × 3,45 м · шифт 2,10 м

OZOD JAMOL · ДИЗАЙН

ВИЗУАЛ



1. Деворлар — илиқ оқ, силлиқ

2. ТВ девори — оч эман рейкалар


3. Шифт бўйлаб илиқ LED ёруғлик

4. Оч кулранг диван ва кресло

5. Пол — оч эман ламинат

6. Кириш — зиғир рулон парда

Бу расм — материал ва кайфият намунаси. Жиҳозлар жойи — 3-бетдаги режа бўйича

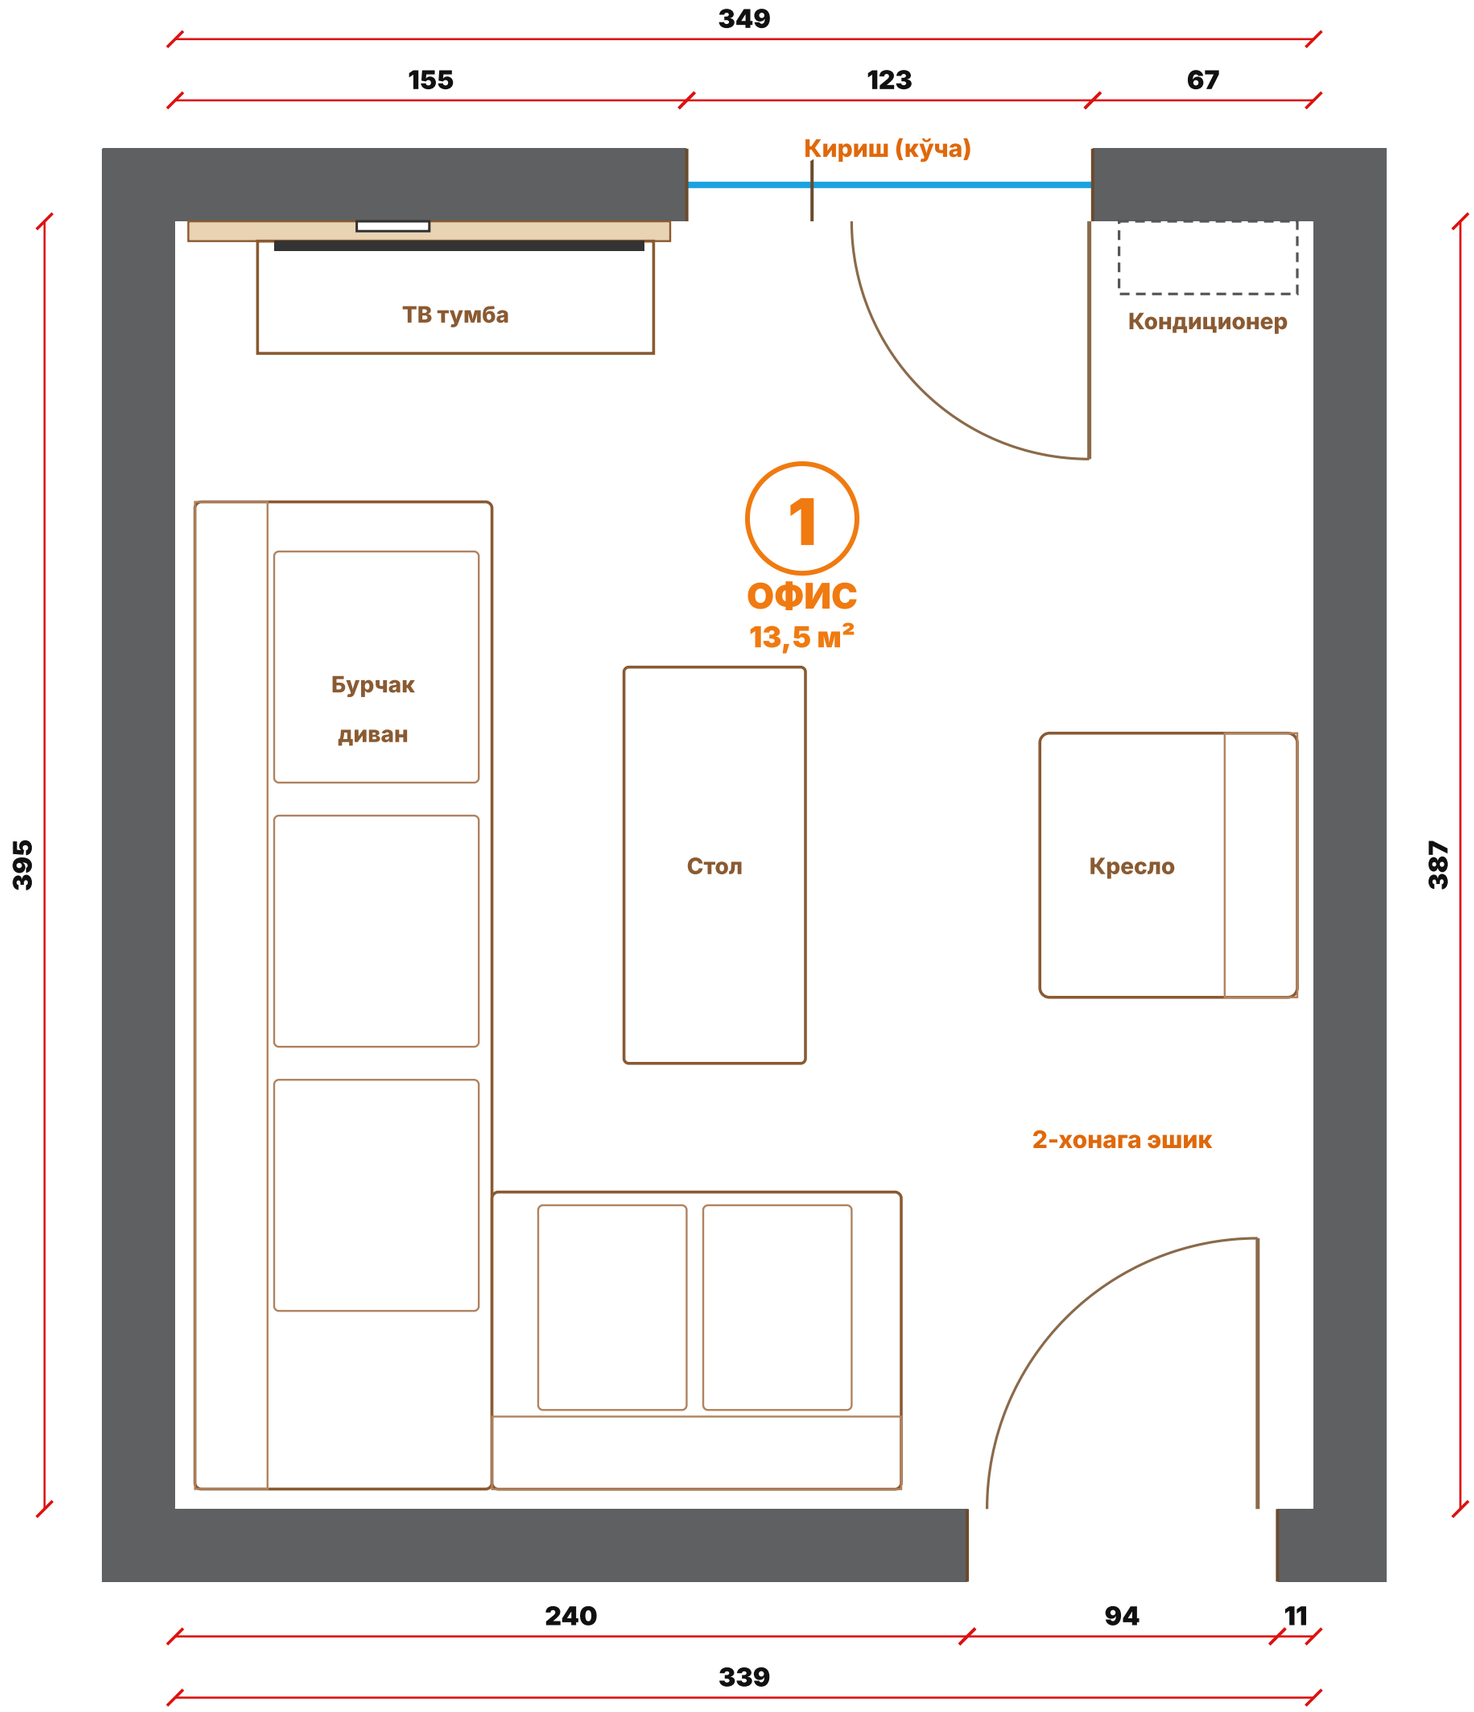

OZOD JAMOL ЧИЗМАСИ

Офис · 13,5 м² · H=210

Умумий жойлашув · М 1:25

Шартли белгилар

- Ойна
- Мебел
- Ўлчам, см
- Рейка + LED H=205 / H=5

H — полдан баландлик, см

Дизайнер: Озод Жамол

Эслатма


1. Ўлчамларни объектнинг ўзида текшириб олинсин.
2. Деворлар 90° эмас — бурчаклар жойида текширилсин.

ВАРАҚ 1

OZOD JAMOL ЧИЗМАСИ

Офис · 13,5 м² · H=210

Электр чизмаси · M 1:25

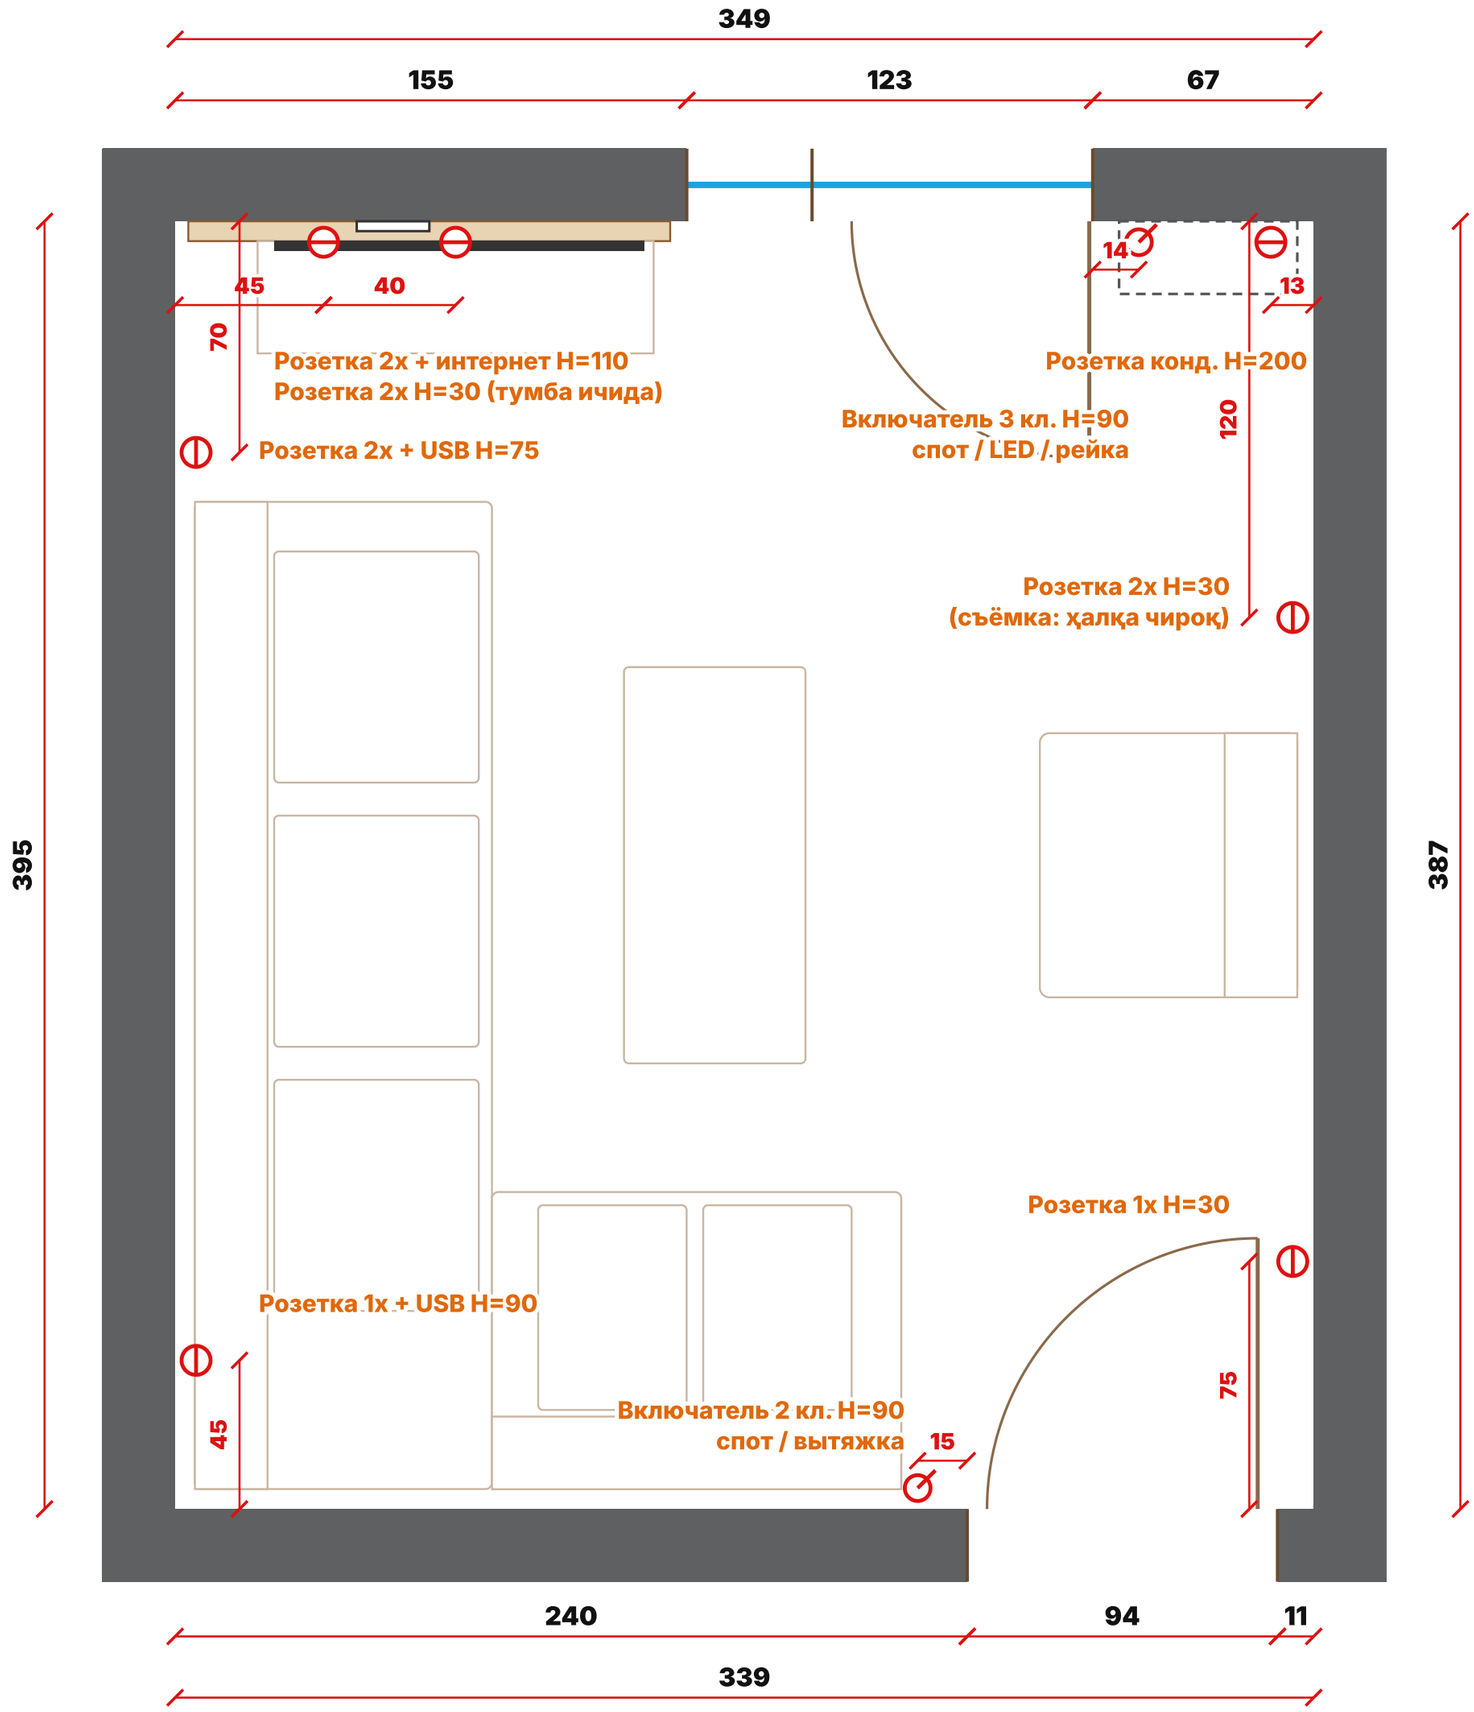

Шартли белгилар

- Розетка
- Включатель
- Ойна
- Ўлчам, см
- Рейка + LED H=205 / H=5


H — полдан баландлик, см

Дизайнер: Озод Жамол

Эслатма

1. Ўлчамларни объектнинг ўзида текшириб олинсин.
2. Кабел фақат вертикал ва горизонтал ётқизилсин.
3. Розетка 11, USB 2, интернет 1.

ВАРАҚ 2

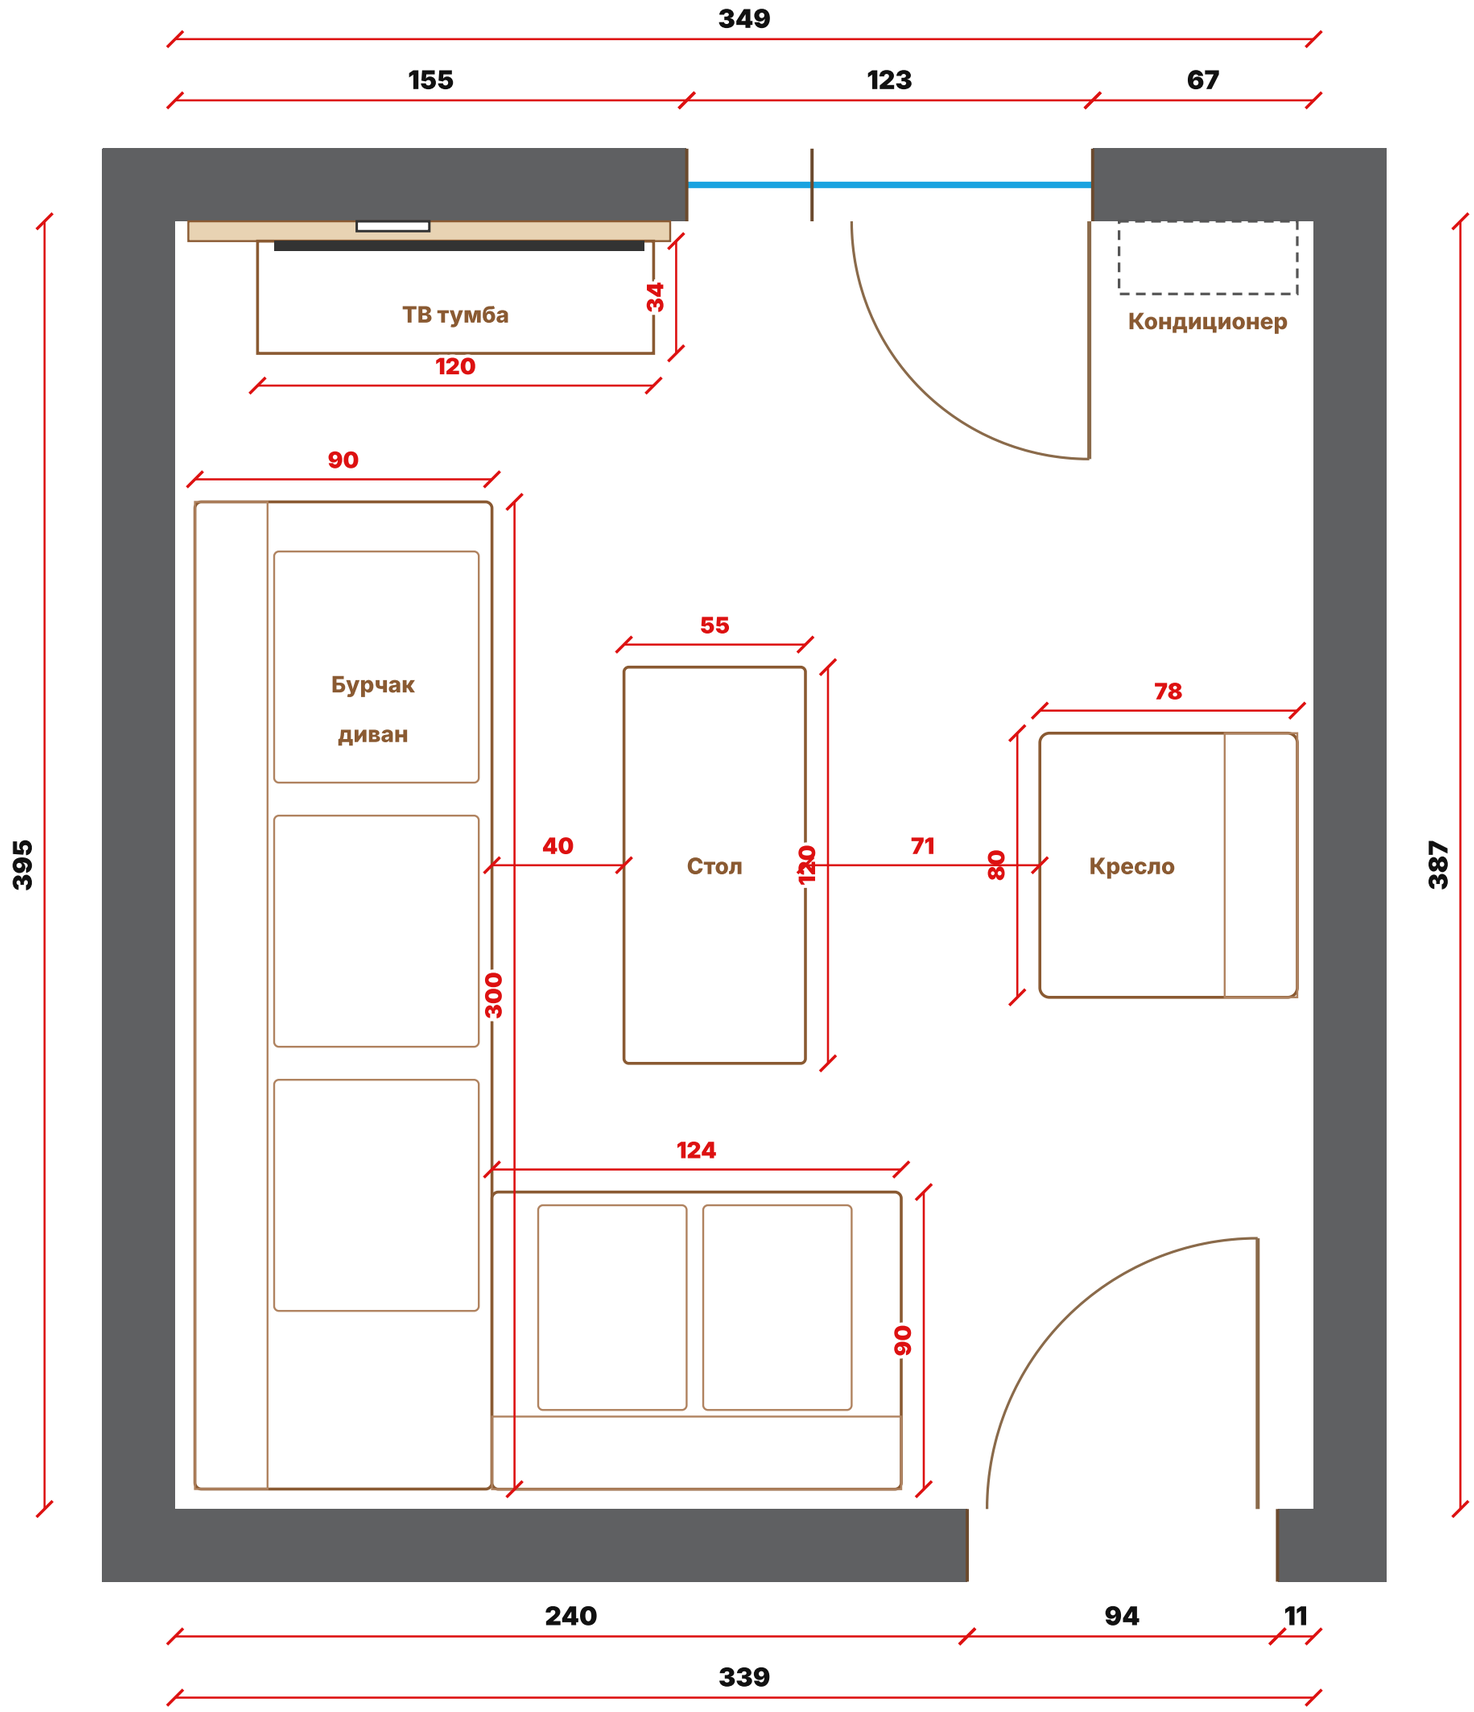

OZOD JAMOL ЧИЗМАСИ

Офис · 13,5 м² · H=210

Мебеллар ўлчамлари · M 1:25

Шартли белгилар

- Мебел
- Ўлчам, см
- Рейка + LED H=205 / H=5


H — полдан баландлик, см

Дизайнер: Озод Жамол


Эслатма

1. Ўлчамларни объектнинг ўзида текшириб олинсин.
2. ТВ 50" (112 см), тумба осма H=28–55.
3. Диван буюртмаси жойида ўлчангач берилсин.
4. Ўтиш йўллари камида 70 см.

ВАРАҚ 3

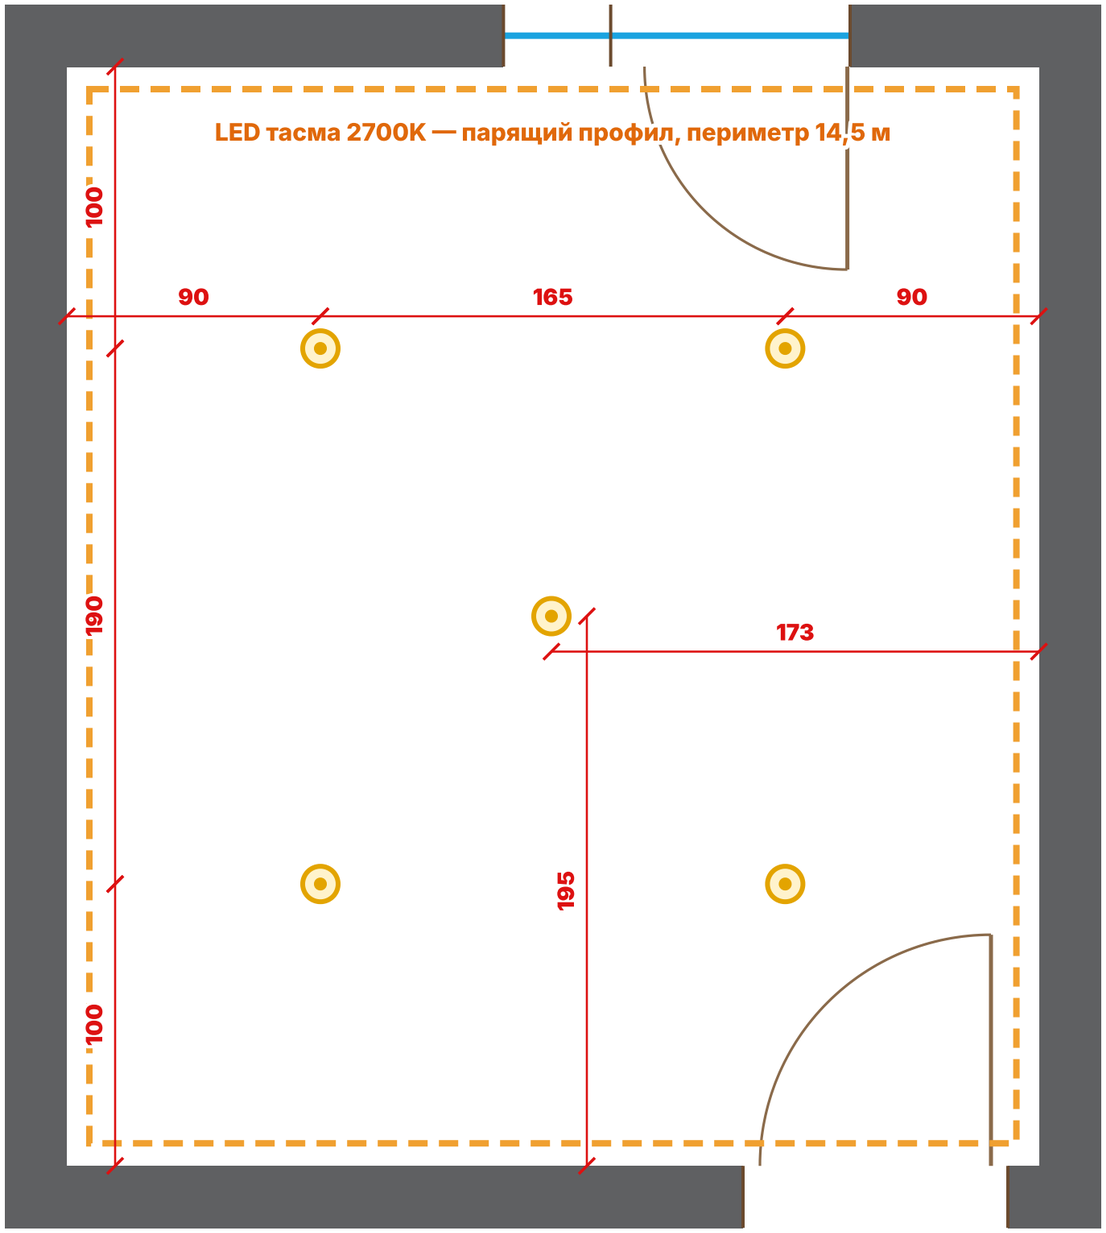

Разрез А-А

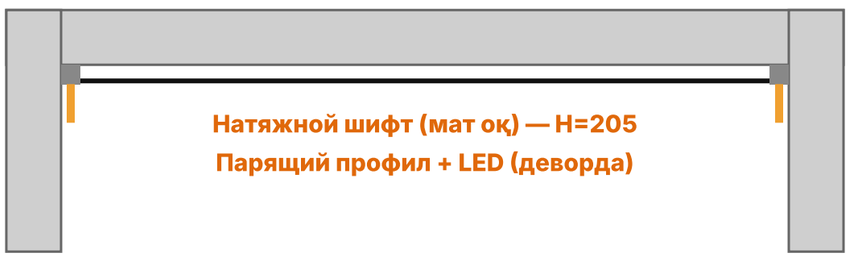

OZOD JAMOL ЧИЗМАСИ

Офис · 13,5 м² · H=210

Шифт чизмаси · M 1:30

Шартли белгилар

- Спот LED 7 Вт, 3000K
- LED тасма 2700K
- Ўлчам, см

H — полдан баландлик, см

Дизайнер: Озод Жамол

Эслатма

1. Ўлчамларни объектнинг ўзида текшириб олинсин.
2. Натяжной шифт 5 см пасаяди: H=205.
3. Спот трансформатори шифт ичида, очиладиган жойда.

ВАРАҚ 4

OZOD JAMOL ЧИЗМАСИ


Офис · 13,5 м² · H=210

ТВ девори ёйилмаси · М 1:20

Шартли белгилар

- Розетка
- Включатель
- Рейка + LED H=205 / H=5
- Ўлчам, см

H — полдан баландлик, см

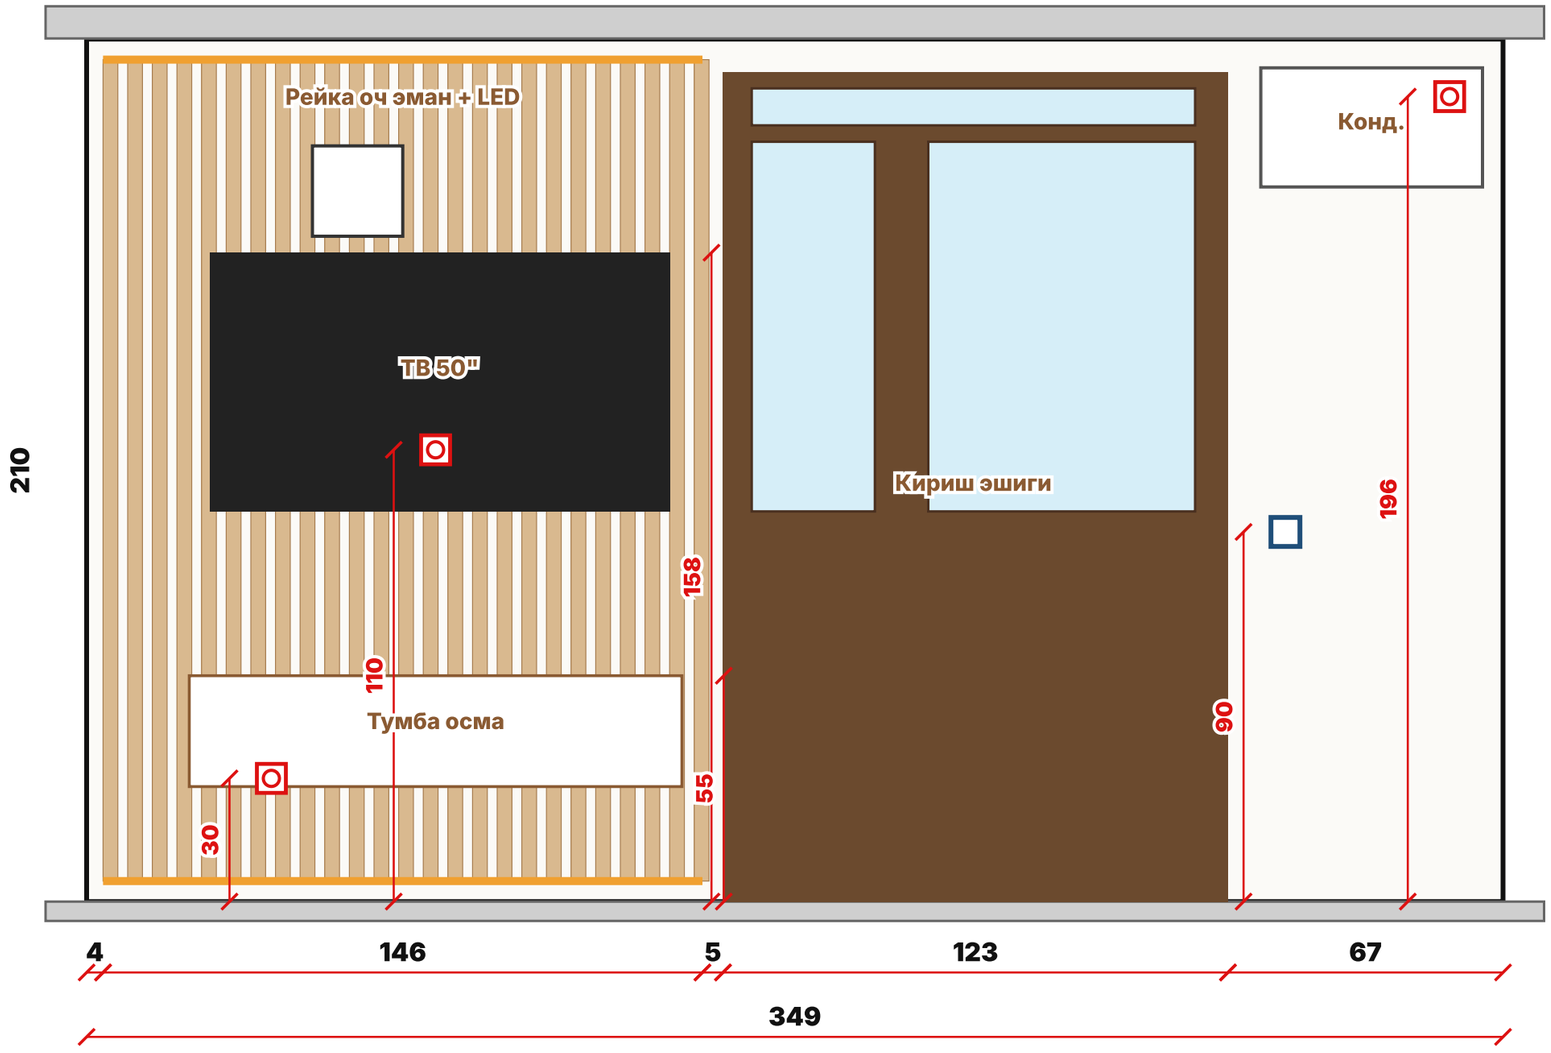

Дизайнер: Озод Жамол

Эслатма

1. Ўлчамларни объектнинг ўзида текшириб олинсин.
2. Розетка ва кабеллар рейка ўрнатилишидан олдин чиқарилсин.
3. ТВ кронштейни учун девор мустаҳкамлансин.

ВАРАҚ 5

РАНГЛАР ВА МАТЕРИАЛЛАР

Деворлар
Илиқ оқ
#F2EEE6

Пол
Оч эман ламинат
#D3B48C

Ёстиқлар
Графит
#5B5B5E

Ёруғлик
2700–3000K
#FFD39A

Рейка, тумба
Оч эман
#C9A27C

Диван, кресло
Оч кулранг
#BDBBB6

Парда
Зиғир
#D8CCB6

Гул
Яшил
#4E6B3A

Ламинат 33 класс, оч эман	15 м²
Плинтус	13 м
Девор бўёғи, илиқ оқ, мат	5 л (2 қават)
Рейкали панел MDF, оч эман	1,5 × 2,1 м
Натяжной шифт, мат оқ	13,5 м²
LED тасма 2700K 24V + профил	18 м
Блок питания 24V 150 Вт	2 дона
Спот LED 7 Вт	5 дона
Розетка / USB / интернет	11 / 2 / 1
Ўчиргич 3 + 2 клавиш	1 + 1
Рулон парда, зиғир	1,25 × 2,2 м

Натяжной шифт 3–5 см пасайтиради — шифт 2,05 м бўлади